






FRONT ELEVATION

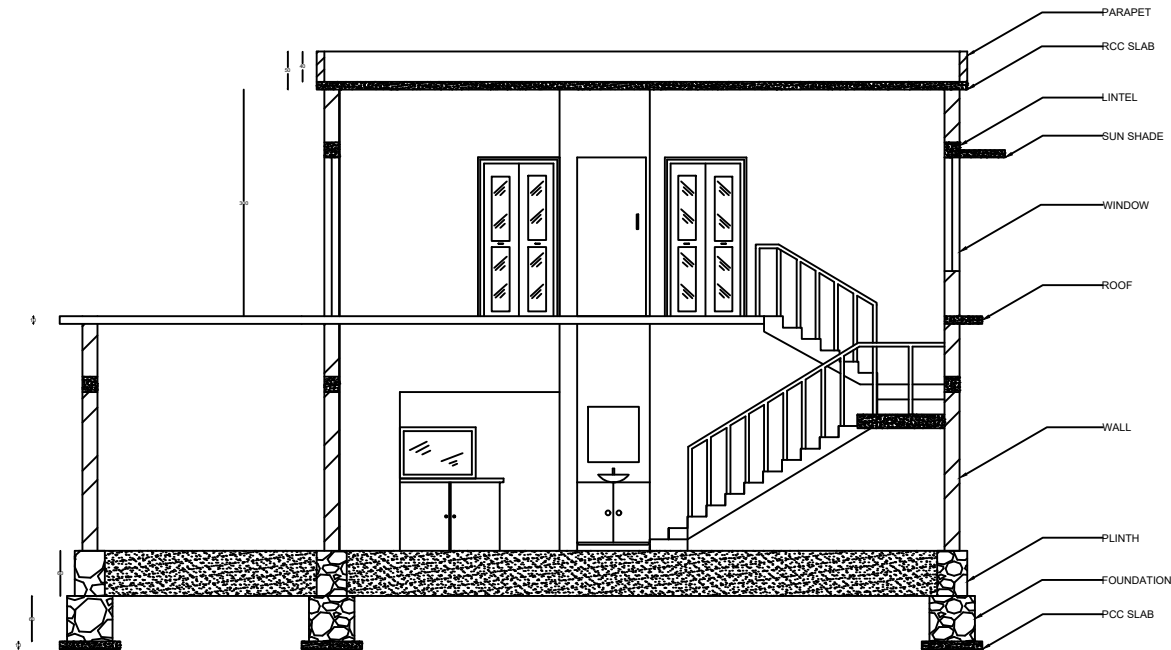

SECTION-AA

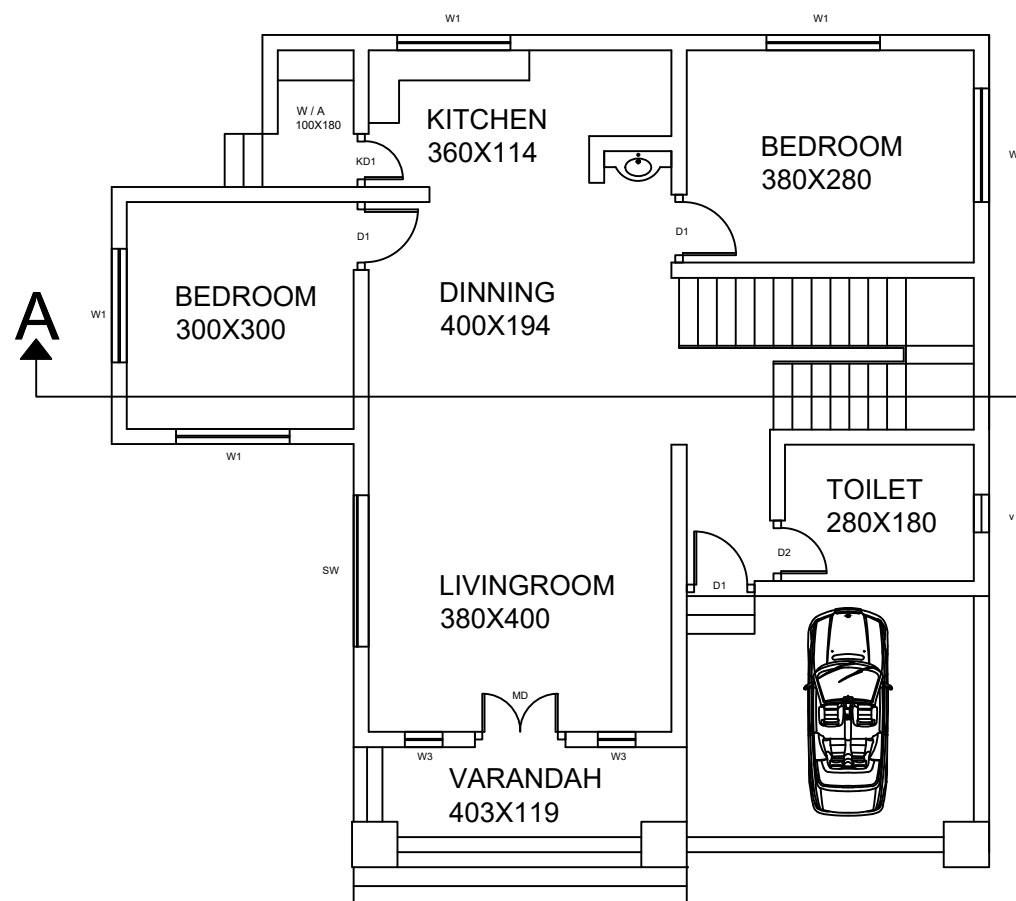

GROUND FLOOR

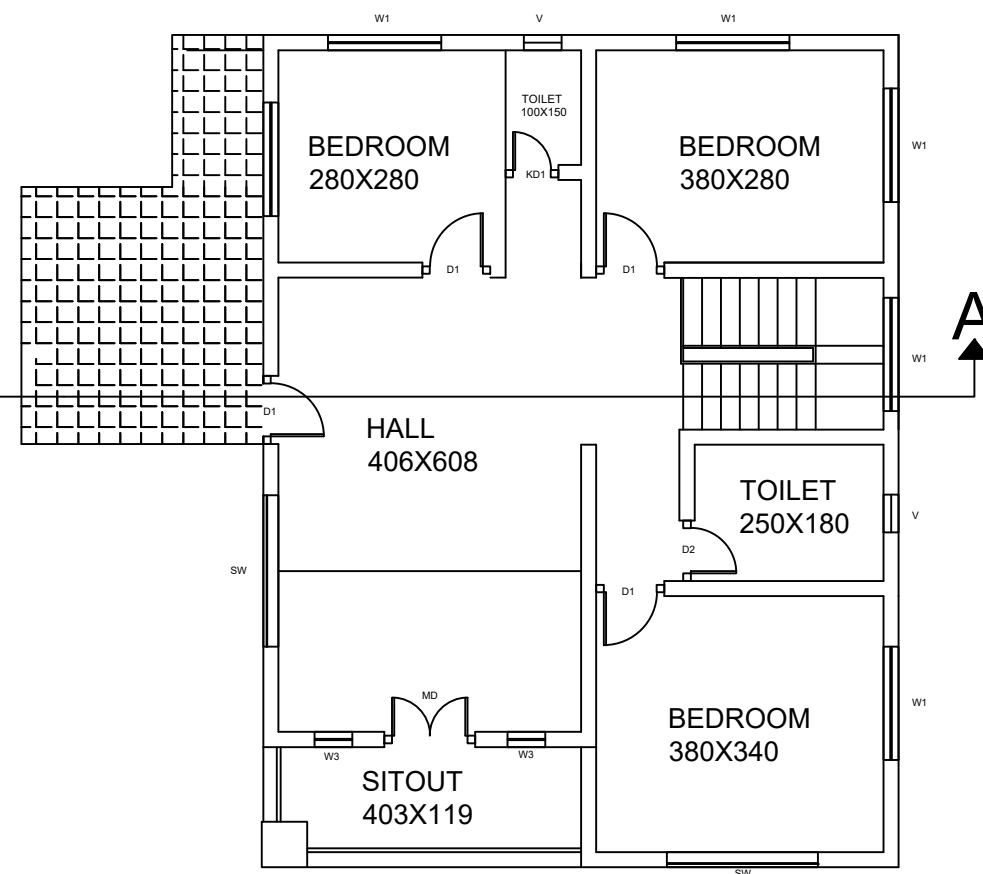

FIRST FLOOR

PROPOSD RESIDENTIAL
BUILDING

SPECIFICATION

ITEM	ID	SIZE
MAINDOOR	MD	120X210
DOOR 1	D1	90X210
DOOR 2	D2	80X210
WINDOW 1	W1	150X150
WINDOW 3	W2	50X150
SLIDING WINDOW	SW	200X150
VENTILATOR	V1	50X50

AREA DETAILS

TYPE	AREA
GF	976.044859 SQ.FT
FF	998.035657 SQ.FT
TOTAL	1974 SQ.FT

STAIR DETAILS

RISE	15 CM
THREAD	25 CM
WIDTH	90 CM

SCALE 1:100
ALL DIMENSIONS ARE IN CM
WALL THICKNESS 20 CM

DRAWN BY :
MUHAMMED MUBASHER

CHECKED BY :
AYSHATH ZUNAF

CADD
CENTRE